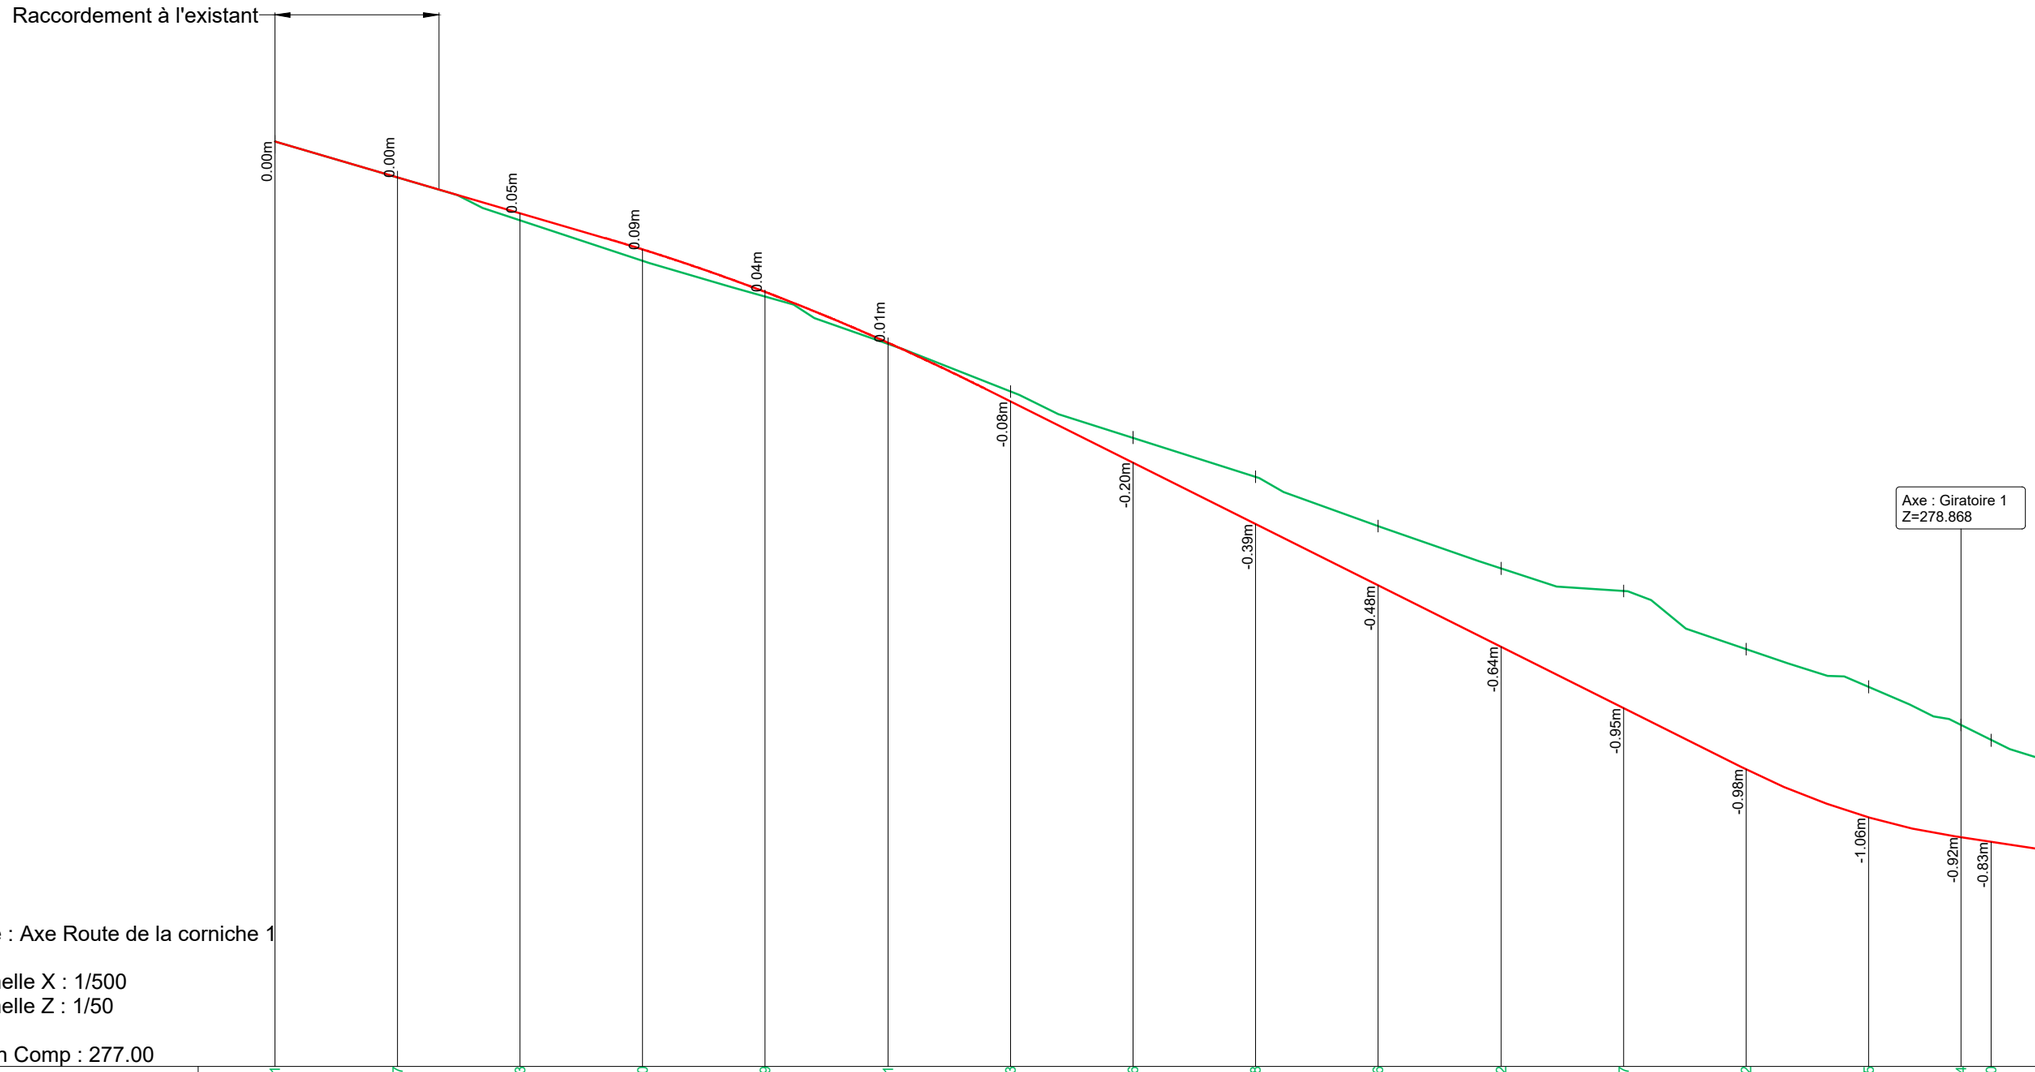

Axe : Axe Route de la corniche 1

Echelle X : 1/500
Echelle Z : 1/50

Plan Comp : 277.00

Terrain	284.541	284.247	283.903	283.570	283.279	282.891	282.503	282.126	281.808	281.406	281.062	280.877	280.402	280.095	279.784	279.660	279.326	278.934	278.867	
Projet Linéaire	284.541	284.249	283.957	283.661	283.314	282.901	282.422	281.922	281.422	280.922	280.422	279.922	279.423	279.031	278.868	278.831	278.681	278.531	278.493	
Distances cumulées	0	10	20	30	40	50	60	70	80	90	100	110	120	130	138	140	150	160	163	
Pentes et rampes	L = 26.90m		P = 2.925%		L = 31.15m R = -1500.00m		L = 61.65m					P = 5.0%		L = 17.48m R = 500.00m		L = 25.46m		P = 1.5%		
Alignts. et courbes		L = 30.56m					L = 59.61m R = 180.00m			L = 8.04m			L = 25.21m R = 80.00m				L = 39.10m			

Axe : Route de la corniche 1
Z=278.868

Axe : Route de la corniche de Brazzaville
Z=277.951

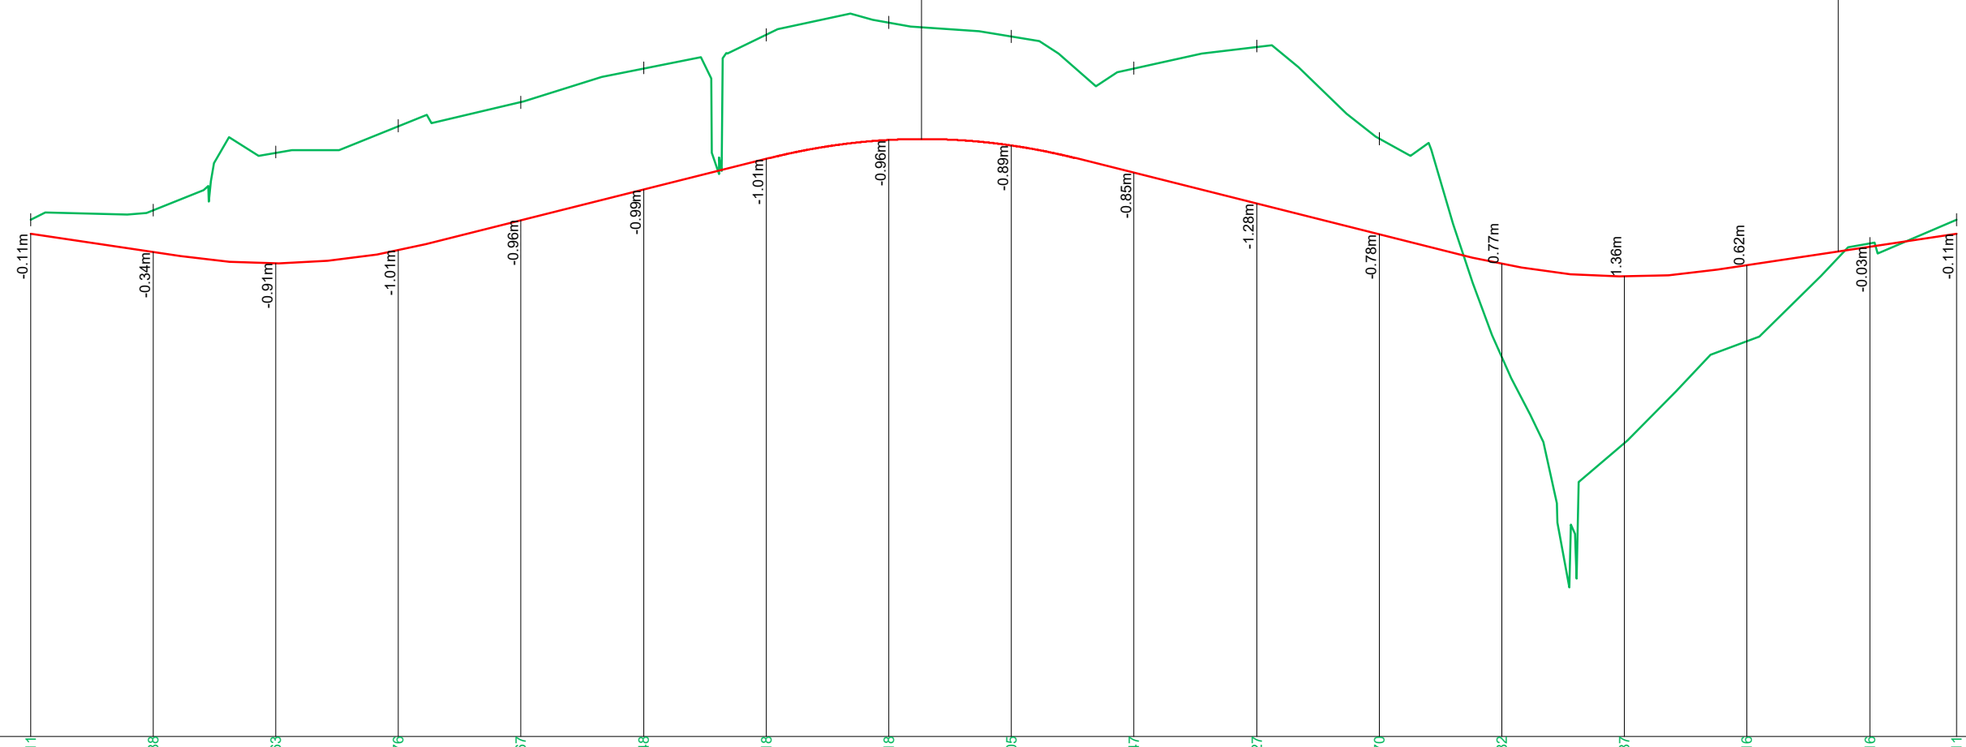

Axe : Giratoire 1

Echelle X : 1/500
Echelle Z : 1/50

Plan Comp : 274.00

Terrain	278.211	278.288	278.763	278.976	279.167	279.448	279.718	279.818	279.705	279.447	279.627	278.870	277.082	276.387	277.216	278.016	278.211
Projet Linéaire	278.096	277.946	277.856	277.961	278.206	278.456	278.706	278.861	278.816	278.593	278.343	278.093	277.849	277.747	277.840	277.990	278.096
Distances cumulées	0	10	20	30	40	50	60	70	80	90	100	110	120	130	140	150	157
Pentes et rampes	P = 1.5% L = 12.25m		L = 20.00m R = 500.00m		L = 28.01m P = 2.5%			L = 25.00m R = -500.00m		L = 32.36m		P = 2.5%		L = 20.00m R = 500.00m		L = 19.49m P = 1.5%	
Alignts. et courbes	L = 157.08m R = 25.00m																

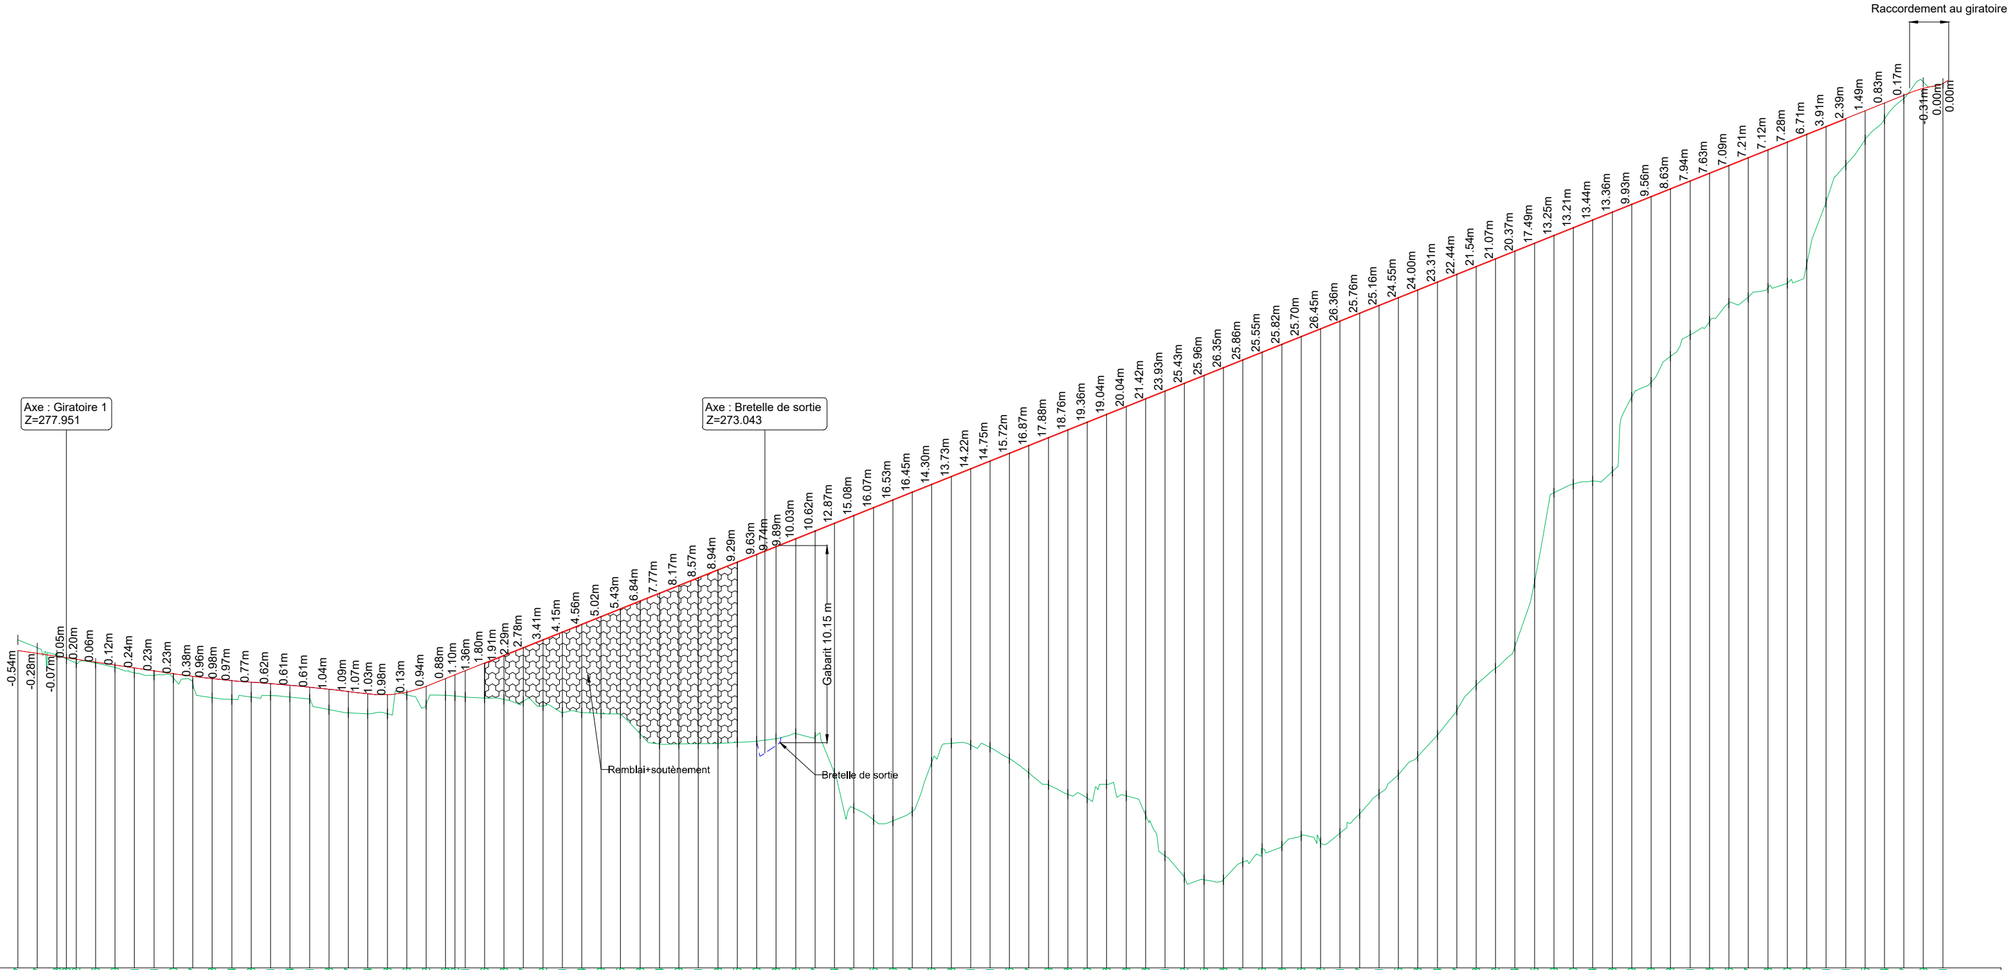

Axe : Route de la corniche de Brazzaville

Echelle X : 1/2500
Echelle Z : 1/250

Plan Comp : 262.00

Terrain	278.867 278.457 278.098 277.898 277.672 277.666 277.459 277.181 277.051 276.900 276.607 275.888 275.804 275.928 276.001 275.924 275.831 275.288 275.127 275.074 275.063 276.038 275.542 276.006 275.982 275.933 275.886 275.798 275.707 275.472 275.141 275.124 275.065 275.055 274.048 273.514 273.519 273.521 273.543 273.595 273.660 273.793 274.052 273.867 272.014 270.207 269.615 269.559 270.037 272.586 273.553 273.461 273.341 272.766 272.017 271.405 270.928 270.730 271.448 270.843 269.863 267.761 266.652 266.525 266.533 267.427 268.136 268.263 268.786 268.432 268.933 269.927 270.931 271.935 272.883 273.974 275.247 276.543 277.412 278.514 281.795 286.435 286.880 287.044 287.528 291.359 292.125 293.458 294.551 295.253 296.196 296.477 296.963 297.210 298.180 301.371 303.291 304.595 305.654 306.717 307.549 307.491
Projet Linéaire	278.326 278.176 278.026 277.951 277.876 277.726 277.576 277.426 277.276 277.126 276.988 276.873 276.774 276.695 276.620 276.535 276.436 276.328 276.216 276.104 276.041 276.164 276.486 276.886 277.080 277.286 277.686 278.086 306.886 307.239 307.549 307.491
Distances cumulées	0 10 20 25 30 40 50 60 70 80 90 100 110 120 130 140 150 160 170 180 190 200 210 220 225 230 240 250 260 270 280 290 300 310 320 330 340 350 360 370 380 390 400 410 420 430 440 450 460 470 480 490 500 510 520 530 540 550 560 570 580 590 600 610 620 630 640 650 660 670 680 690 700 710 720 730 740 750 760 770 780 790 800 810 820 830 840 850 860 870 880 890 900 910 920 930 940 950 960 970 980 990
Pentes et rampes	P = 1.5% L = 80.86m L = 33.03m L = 12.92m R = 3500.00m Profil en long déduit du pont de Djoué L = 25.07m R = 500.00m L = 764.90m P = 4.0% L = 12.43m R = 500.00m
Alignts. et courbes	L = 30.89m R = 250.00m L = 125.50m L = 81.69m R = 250.00m L = 136.41m L = 540.80m R = 450.00m L = 44.67m

Axe : Bretelle de sortie

Echelle X : 1/1500
Echelle Z : 1/150

Plan Comp : 269.00

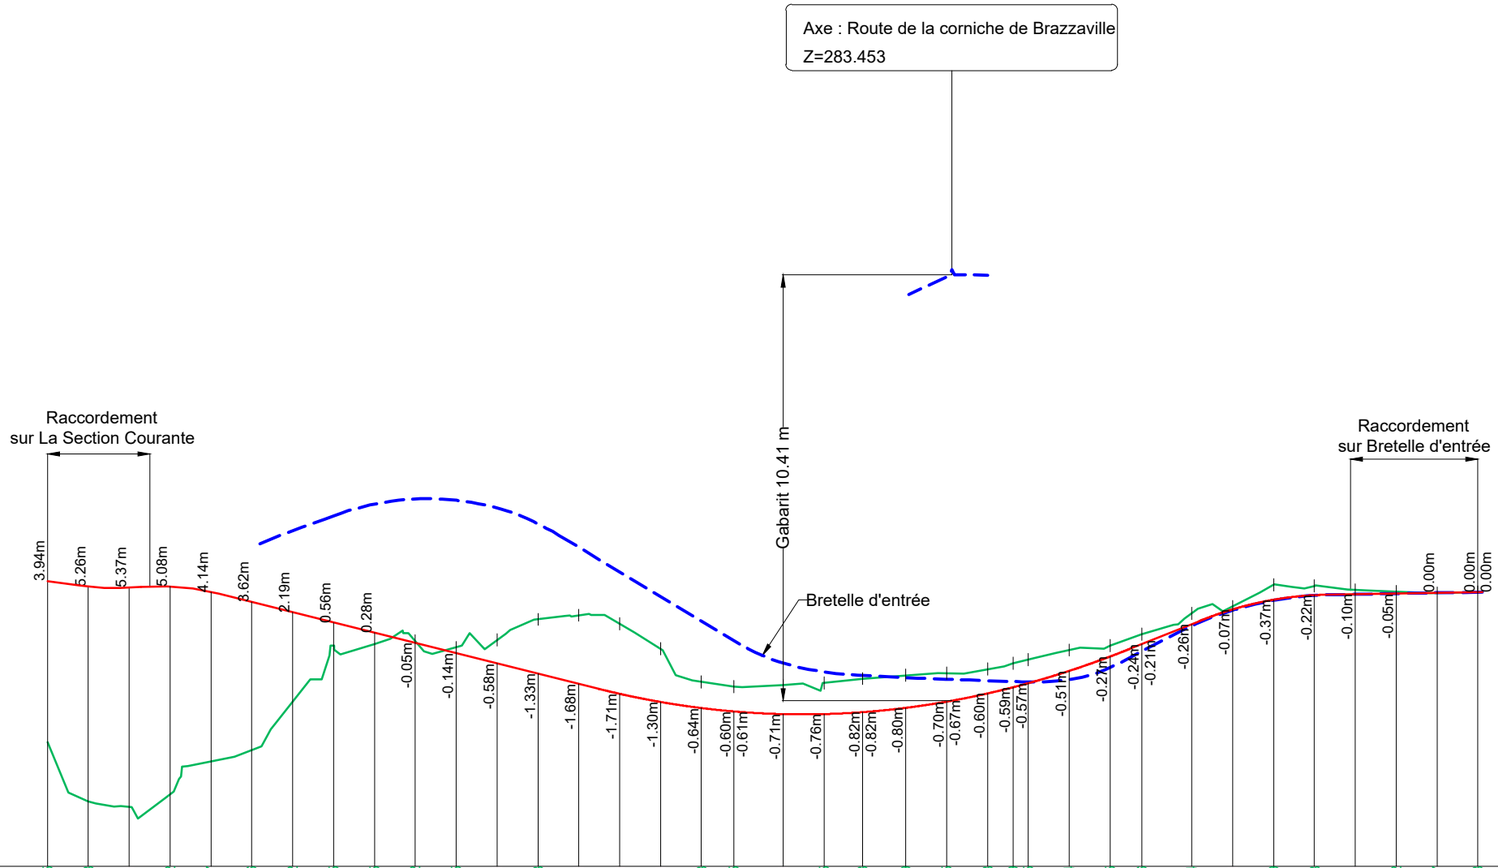

| | | |

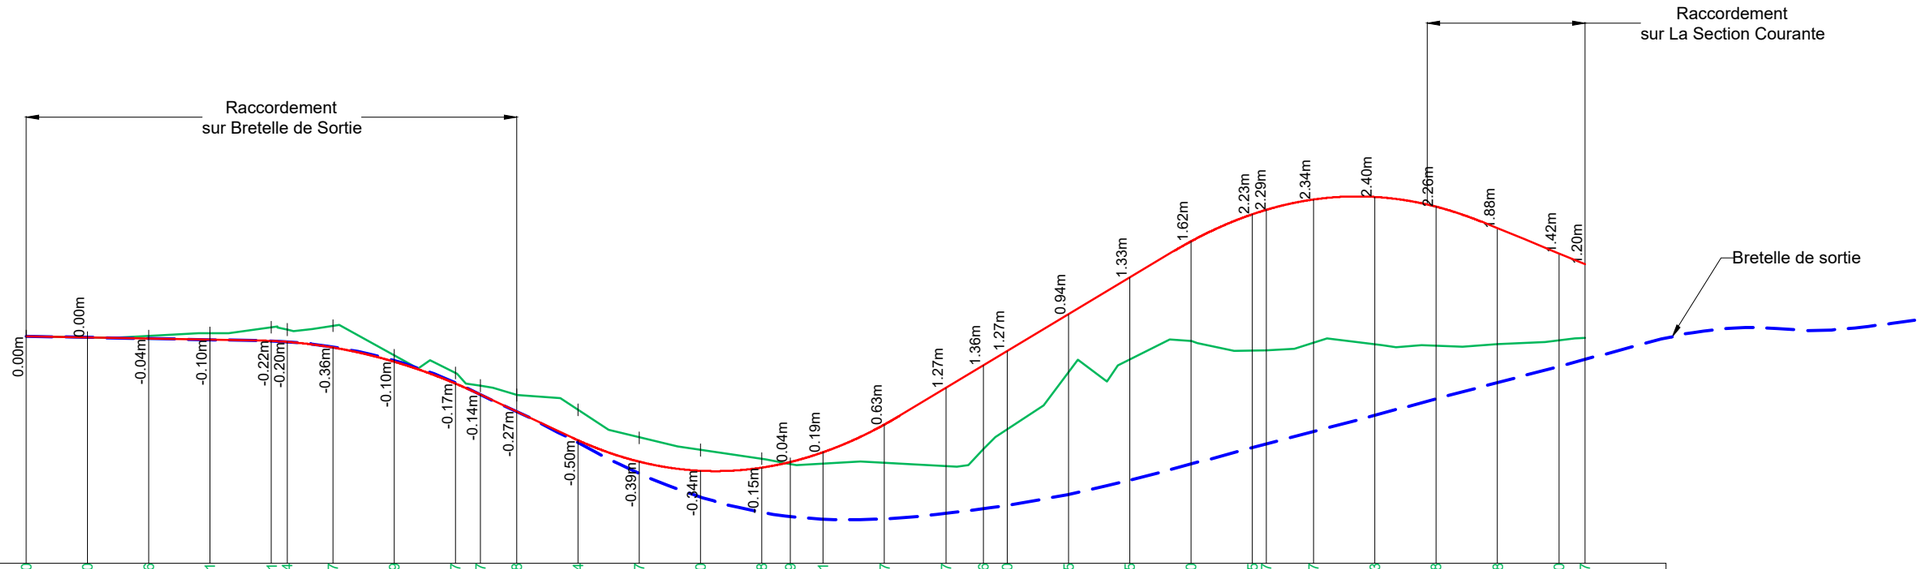

Axe : Bretelle d'entrée

Echelle X : 1/1000
Echelle Z : 1/100

Plan Comp : 272.00

Terrain	275.700 275.680 275.706 275.751 275.851 275.814 275.877 275.389 275.107 274.897 274.748 274.504 274.047 273.850 273.708 273.619 273.621 273.637 273.587 273.866 274.190 275.115 275.325 275.630 275.465 275.477 275.597 275.573 275.558 275.578 275.640 275.677
Projet Linéaire	275.700 275.682 275.665 275.647 275.627 275.612 275.520 275.289 274.933 274.752 274.474 274.008 273.659 273.511 273.562 273.655 273.814 274.265 274.859 275.229 275.459 276.059 276.659 277.251 277.692 277.764 277.933 277.974 277.815 277.463 277.055 276.882
Distances cumulées	0 10 20 30 40 43 50 60 70 74 80 90 100 110 120 125 130 140 150 156 160 170 180 190 200 202 210 220 230 240 250 254
Pentes et rampes	P = 0.176% L = 37.89m; L = 36.03m R = -800.00m; R = 4.677% L = 15.15m; L = 53.41m R = 500.00m; L = 44.78m P = 6.0%; L = 50.29m R = -500.00m; P = 4.077% L = 4.84m; P = 4.077% L = 4.84m; P = 4.075% L = 4.99m; P = 4.073%
Alignts. et courbes	L = 42.56m; L = 31.50m A = 39.686; L = 50.60m R = 50.00m; L = 31.50m A = 39.686; L = 46.11m; L = 51.99m R = 242.50m