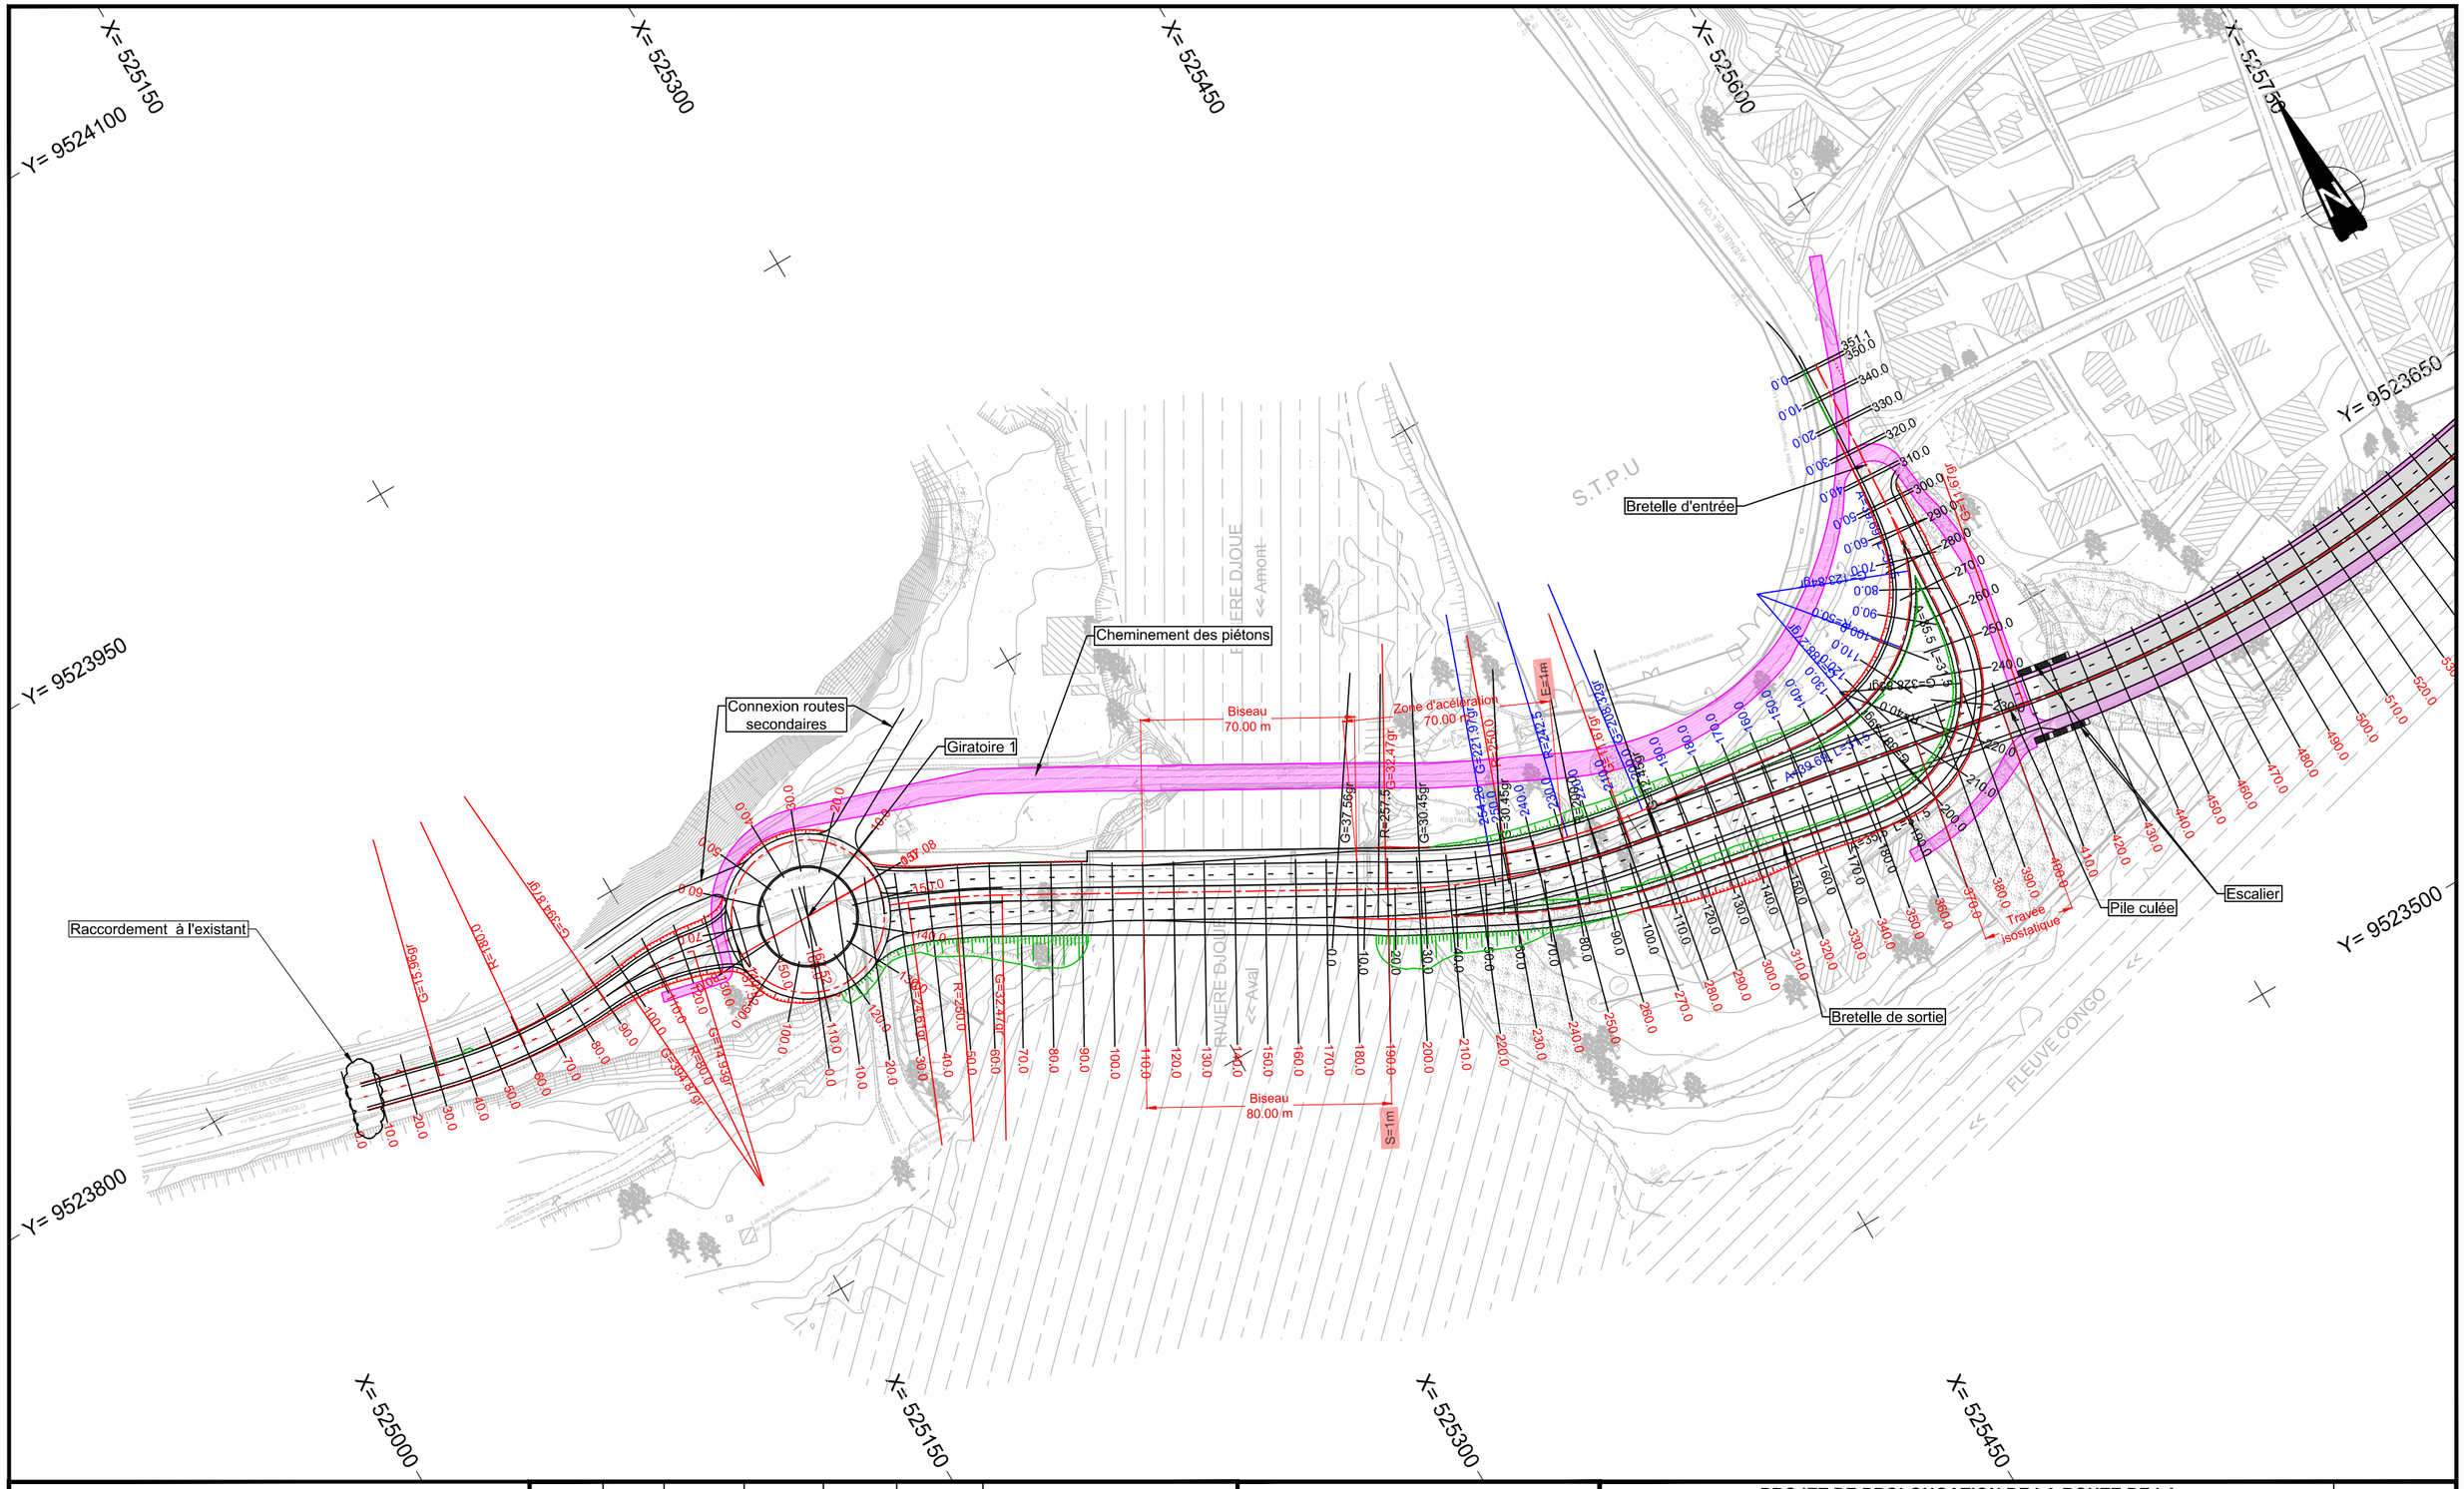

A	0	Jan.2020	FMZ	MMI	JBD	Première émission
Dif.	Rev.	Date	Auteur	Vérif	Approb	Modifications

setec international

setec tpi

STUDI INTERNATIONAL

PROJET DE PROLONGATION DE LA ROUTE DE LA CORNICHE A BRAZZAVILLE

ETUDES D'AMENAGEMENT DU TRONÇON FULBERT YOULOU - PONT DU DJOUE

01

Etude routière
Vue en plan _ Variante 1

ECHELLE : 1/ 2000

Projet	Emetteur	Phase	Type	Numéro	Dif.	Rev
CYBZD	SI	APS	PLA	0101	A	0

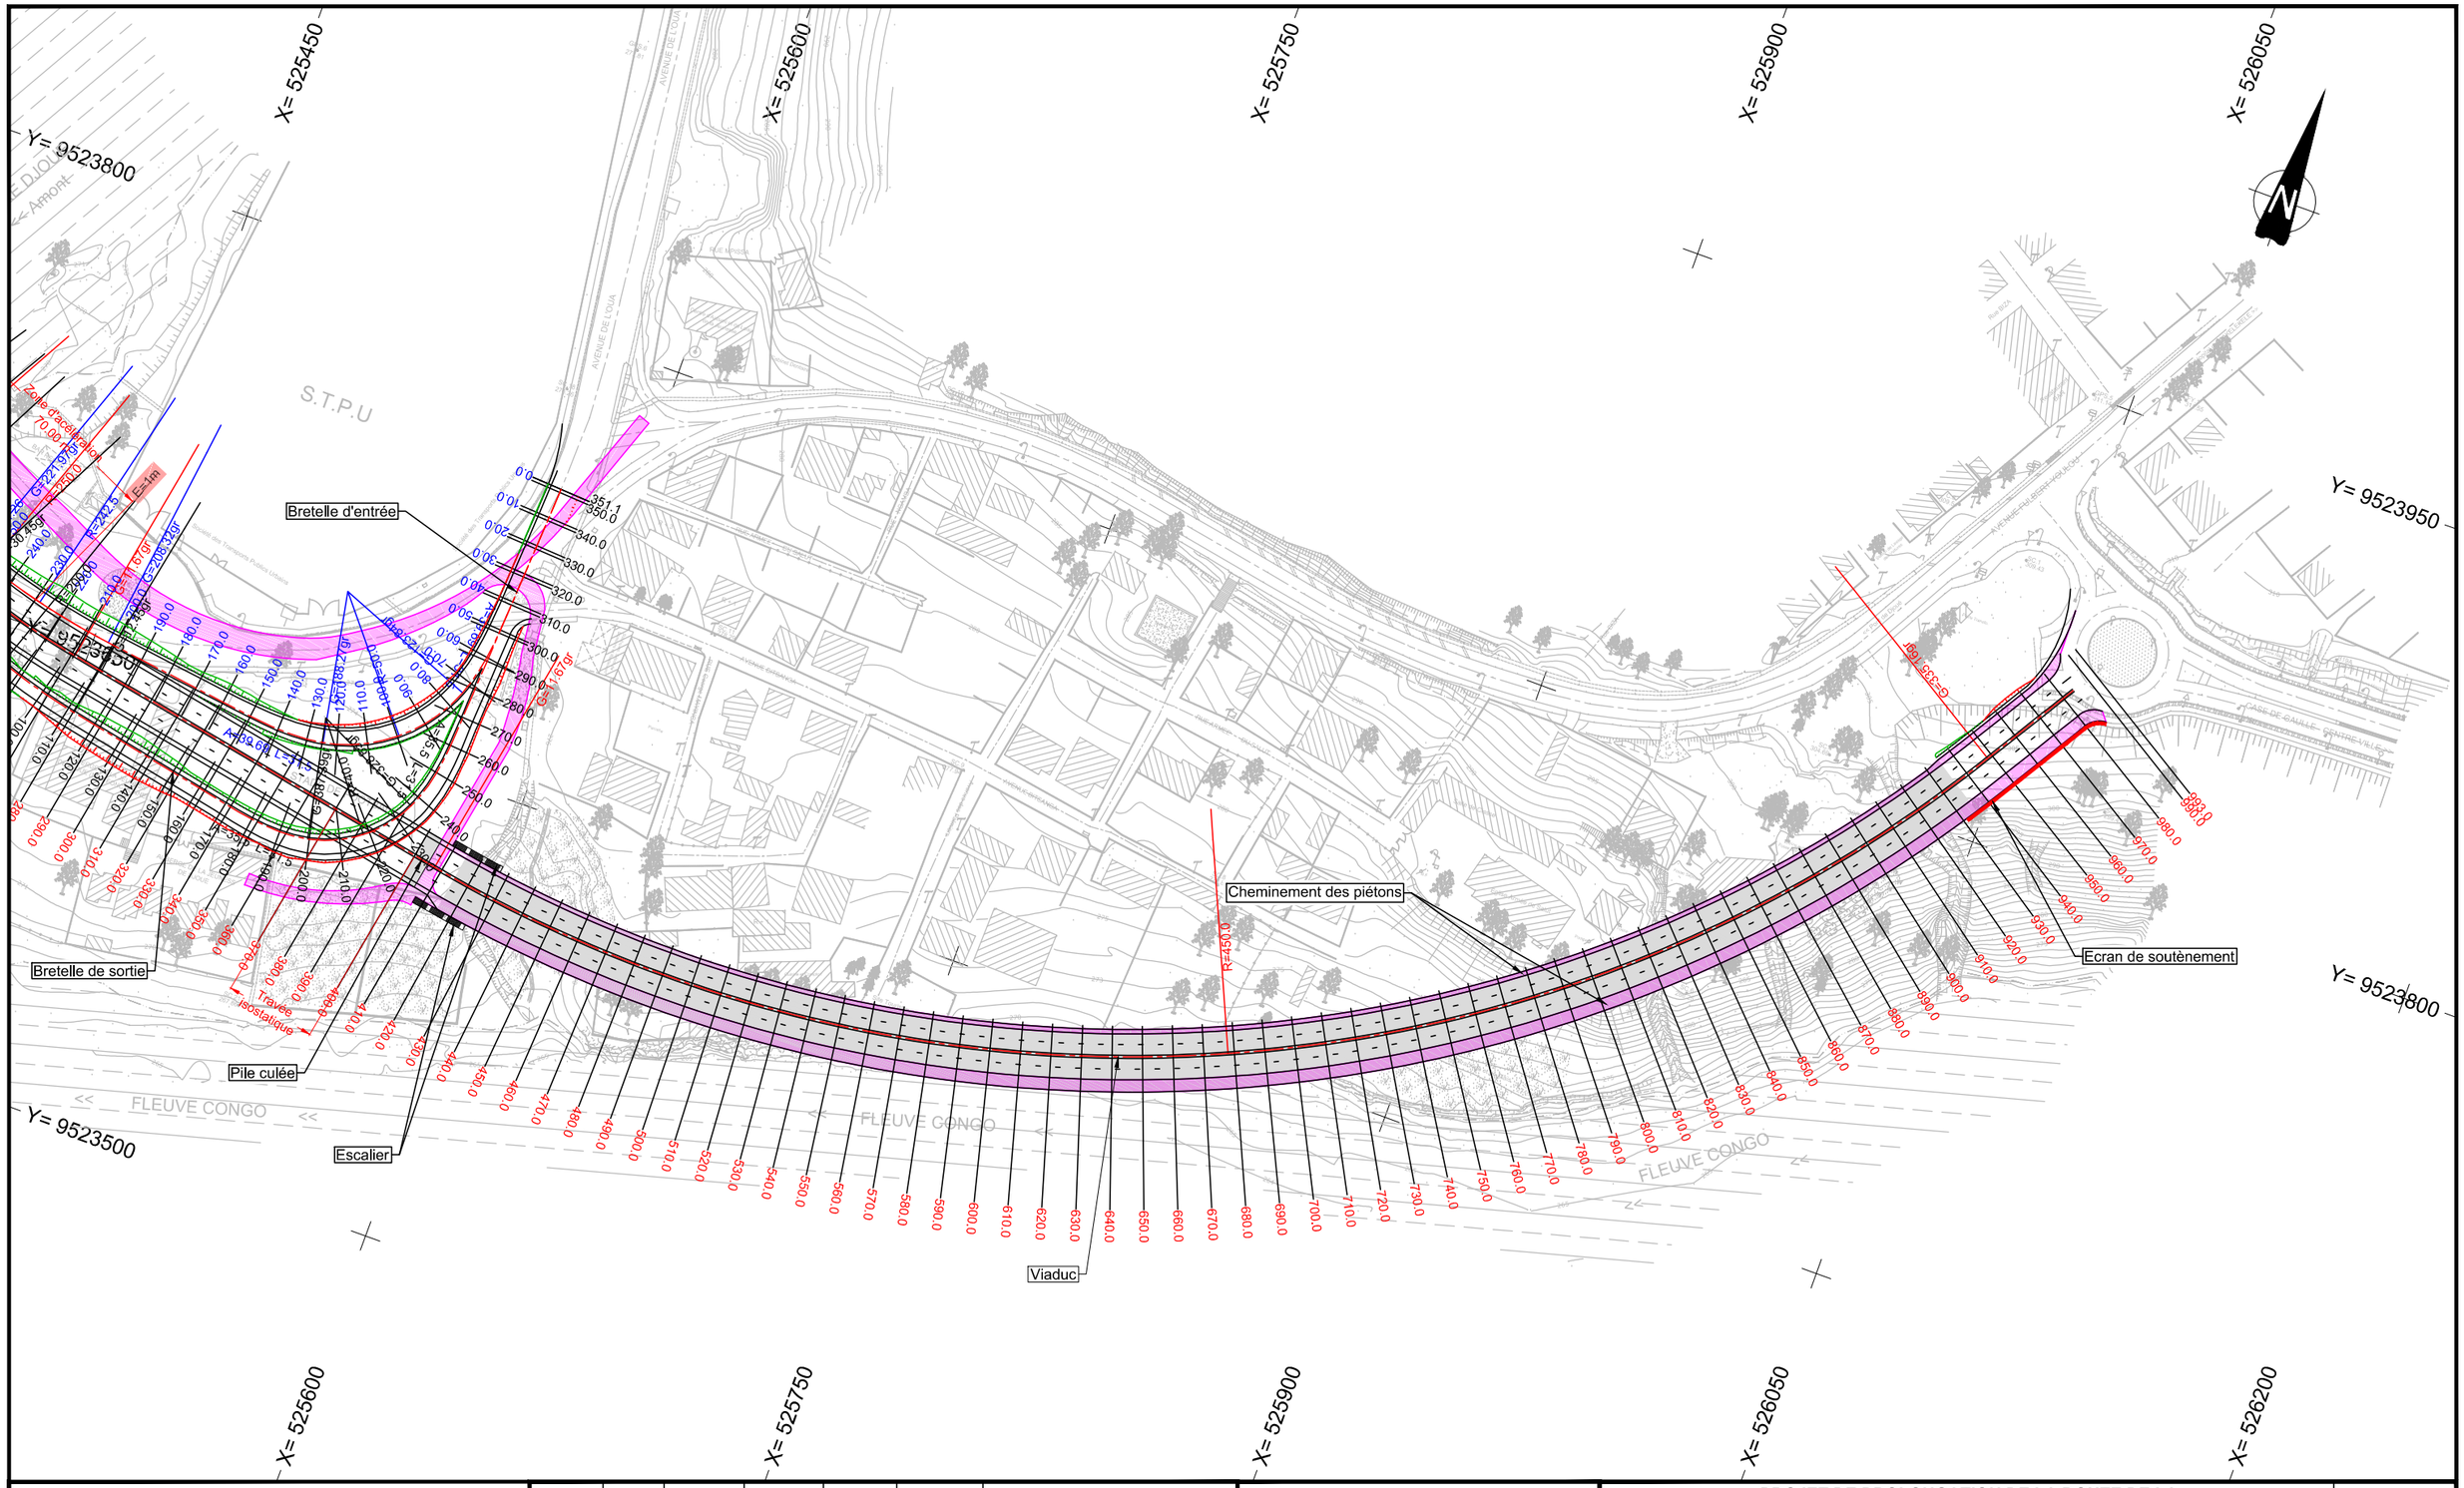

A	0	Jan.2020	FMZ	MMI	JBD	Première émission
Dif.	Rev.	Date	Auteur	Vérif	Approb	Modifications

setec international

setec tpi

STUDI INTERNATIONAL

PROJET DE PROLONGATION DE LA ROUTE DE LA CORNICHE A BRAZZAVILLE

ETUDES D'AMENAGEMENT DU TRONÇON FULBERT YOULOU - PONT DU DJOUE

02

Etude routière
Vue en plan _ Variante 1

ECHELLE : 1/ 2000

Projet	Emetteur	Phase	Type	Numéro	Dif.	Rev
CYBZD	SI	APS	PLA	0101	A	0