Raccordement sur existant

Axe : Axe giratoire 2
Z=276.699

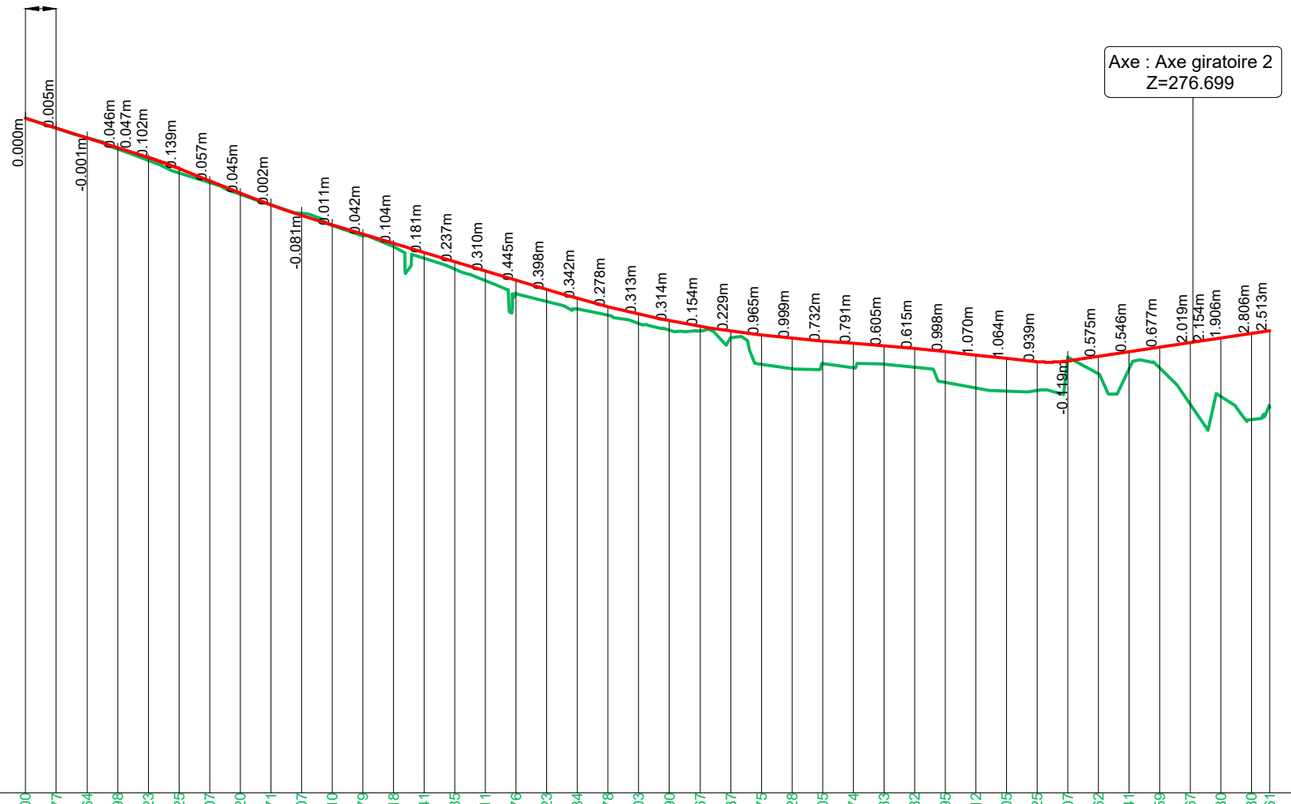

Axe : Route de la corniche de Brazzaville

Echelle X : 1/2000
Echelle Z : 1/200

Plan Comp : 262.00

| | | |

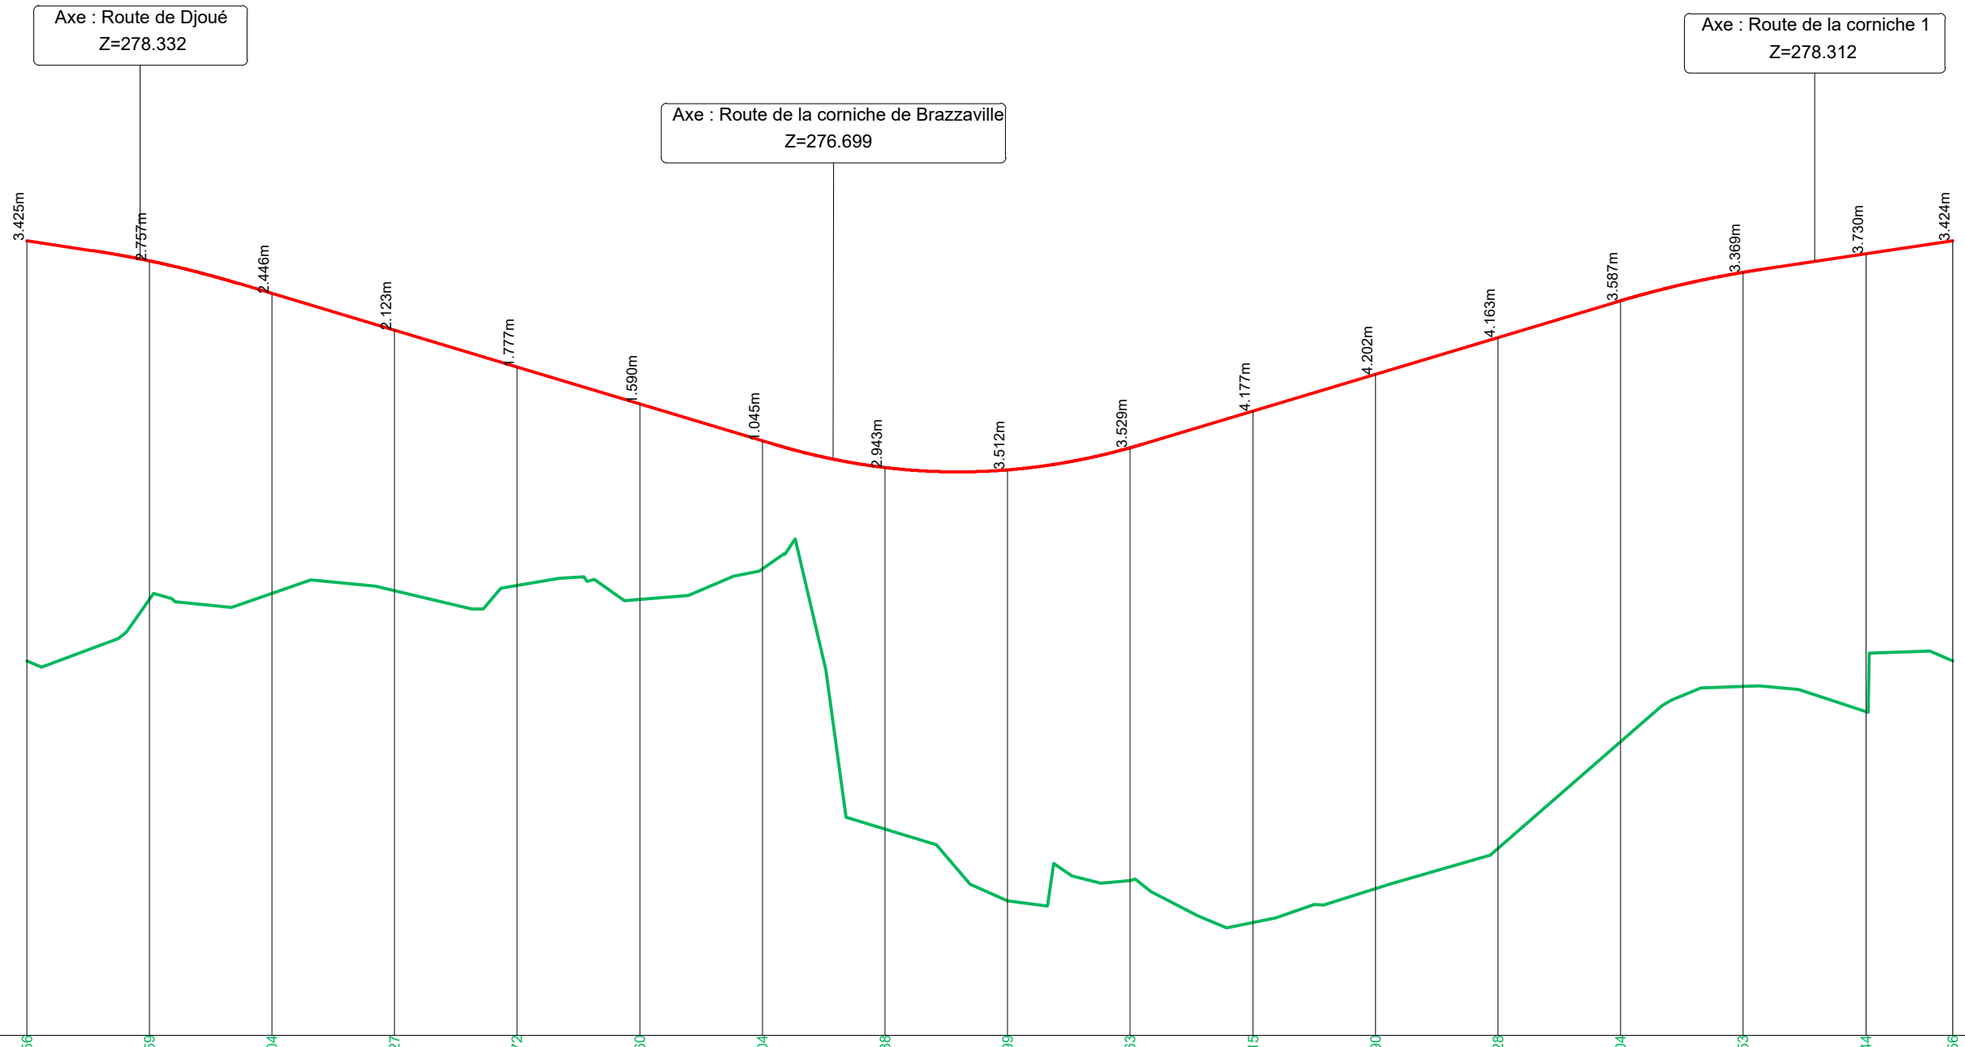

Axe : Axe giratoire 2

Echelle X : 1/500
Echelle Z : 1/50

Plan Comp : 272.00

Terrain	275.056	275.559	275.604	275.627	275.672	275.560	275.804	273.688	273.099	273.263	272.915	273.190	273.528	274.404	274.853	274.644	275.056
Projet Linéaire	278.480	278.316	278.049	277.749	277.449	277.149	276.849	276.631	276.612	276.792	277.092	277.392	277.692	277.991	278.223	278.374	278.480
Distances cumulées	0	10	20	30	40	50	60	70	80	90	100	110	120	130	140	150	157
Pentes et rampes	P = 1.5% L = 5.272m	L = 12.003m R = -800.000m	L = 43.712m				P = 3.0%	L = 30.004m R = 500.000m		L = 38.559m				P = 3.0%	L = 12.003m R = -800.000m	L = 15.573m	P = 1.5%
Alignts. et courbes	L = 157.077m R = 25.000m																

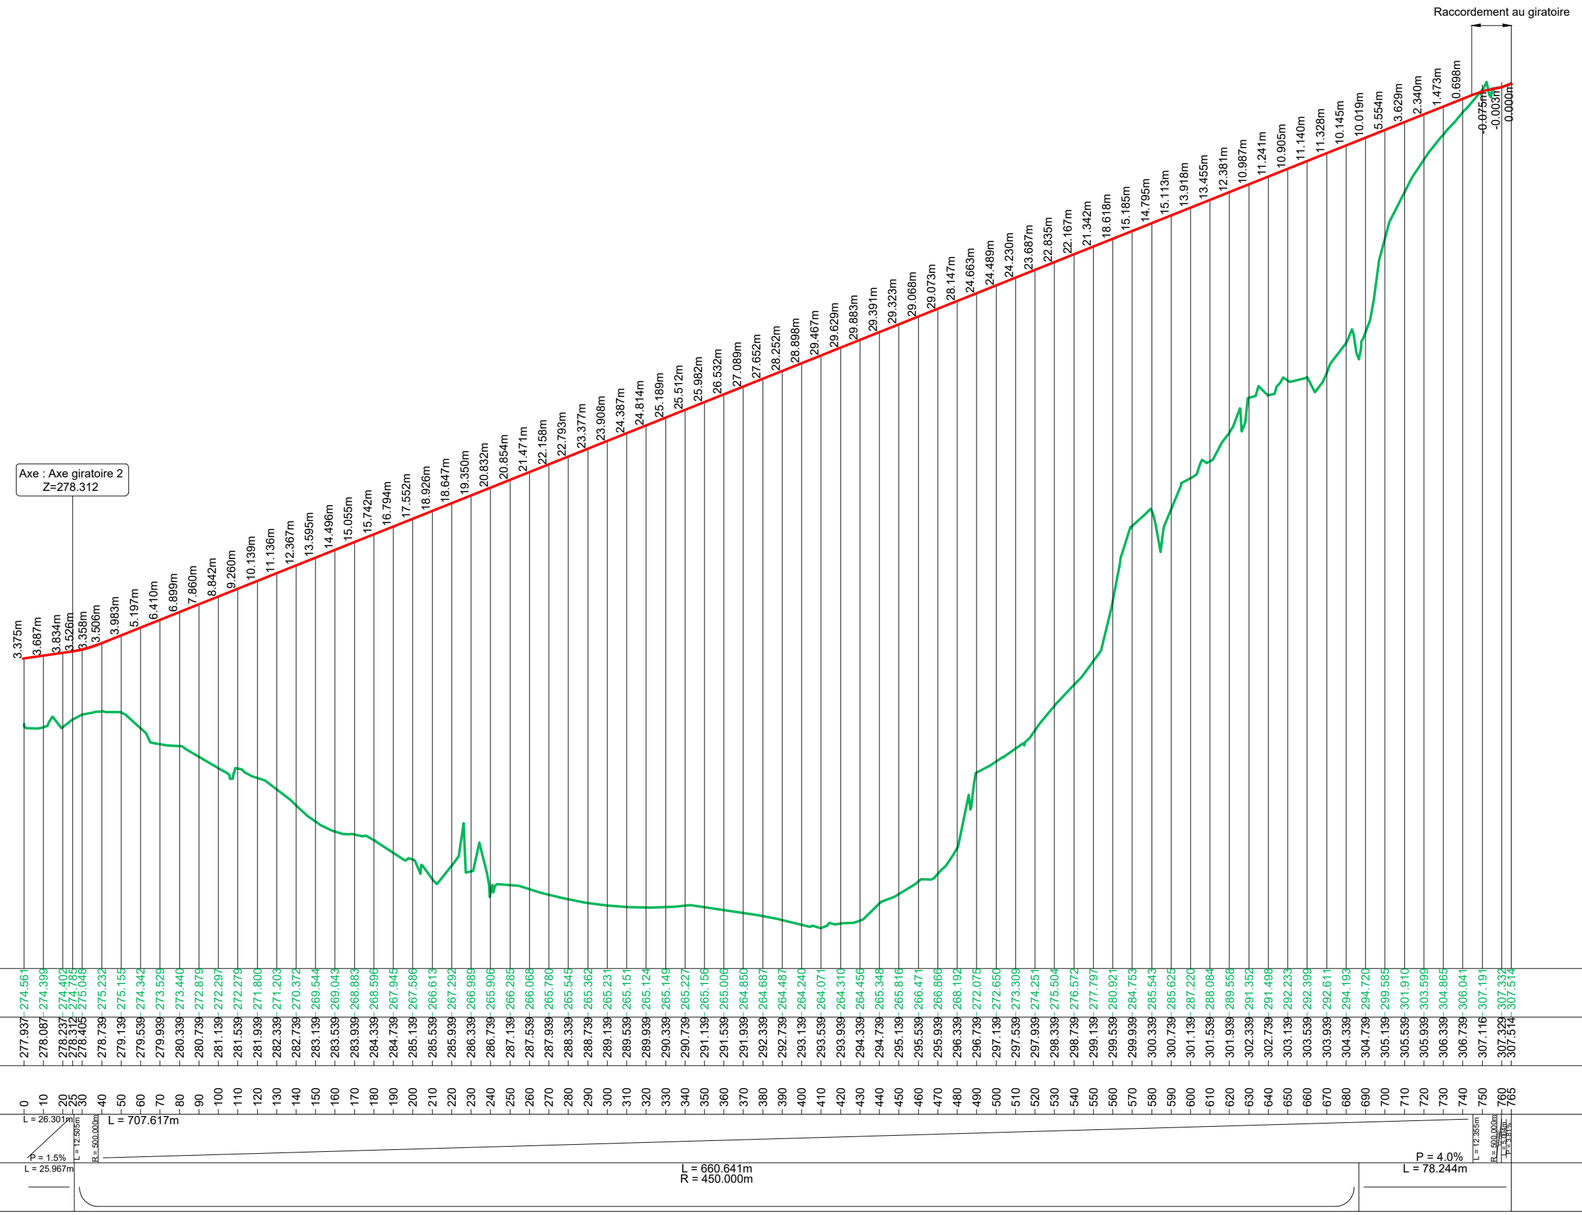

Axe : Route de la corniche 1

Echelle X : 1/2500
Echelle Z : 1/250

Plan Comp : 262.00

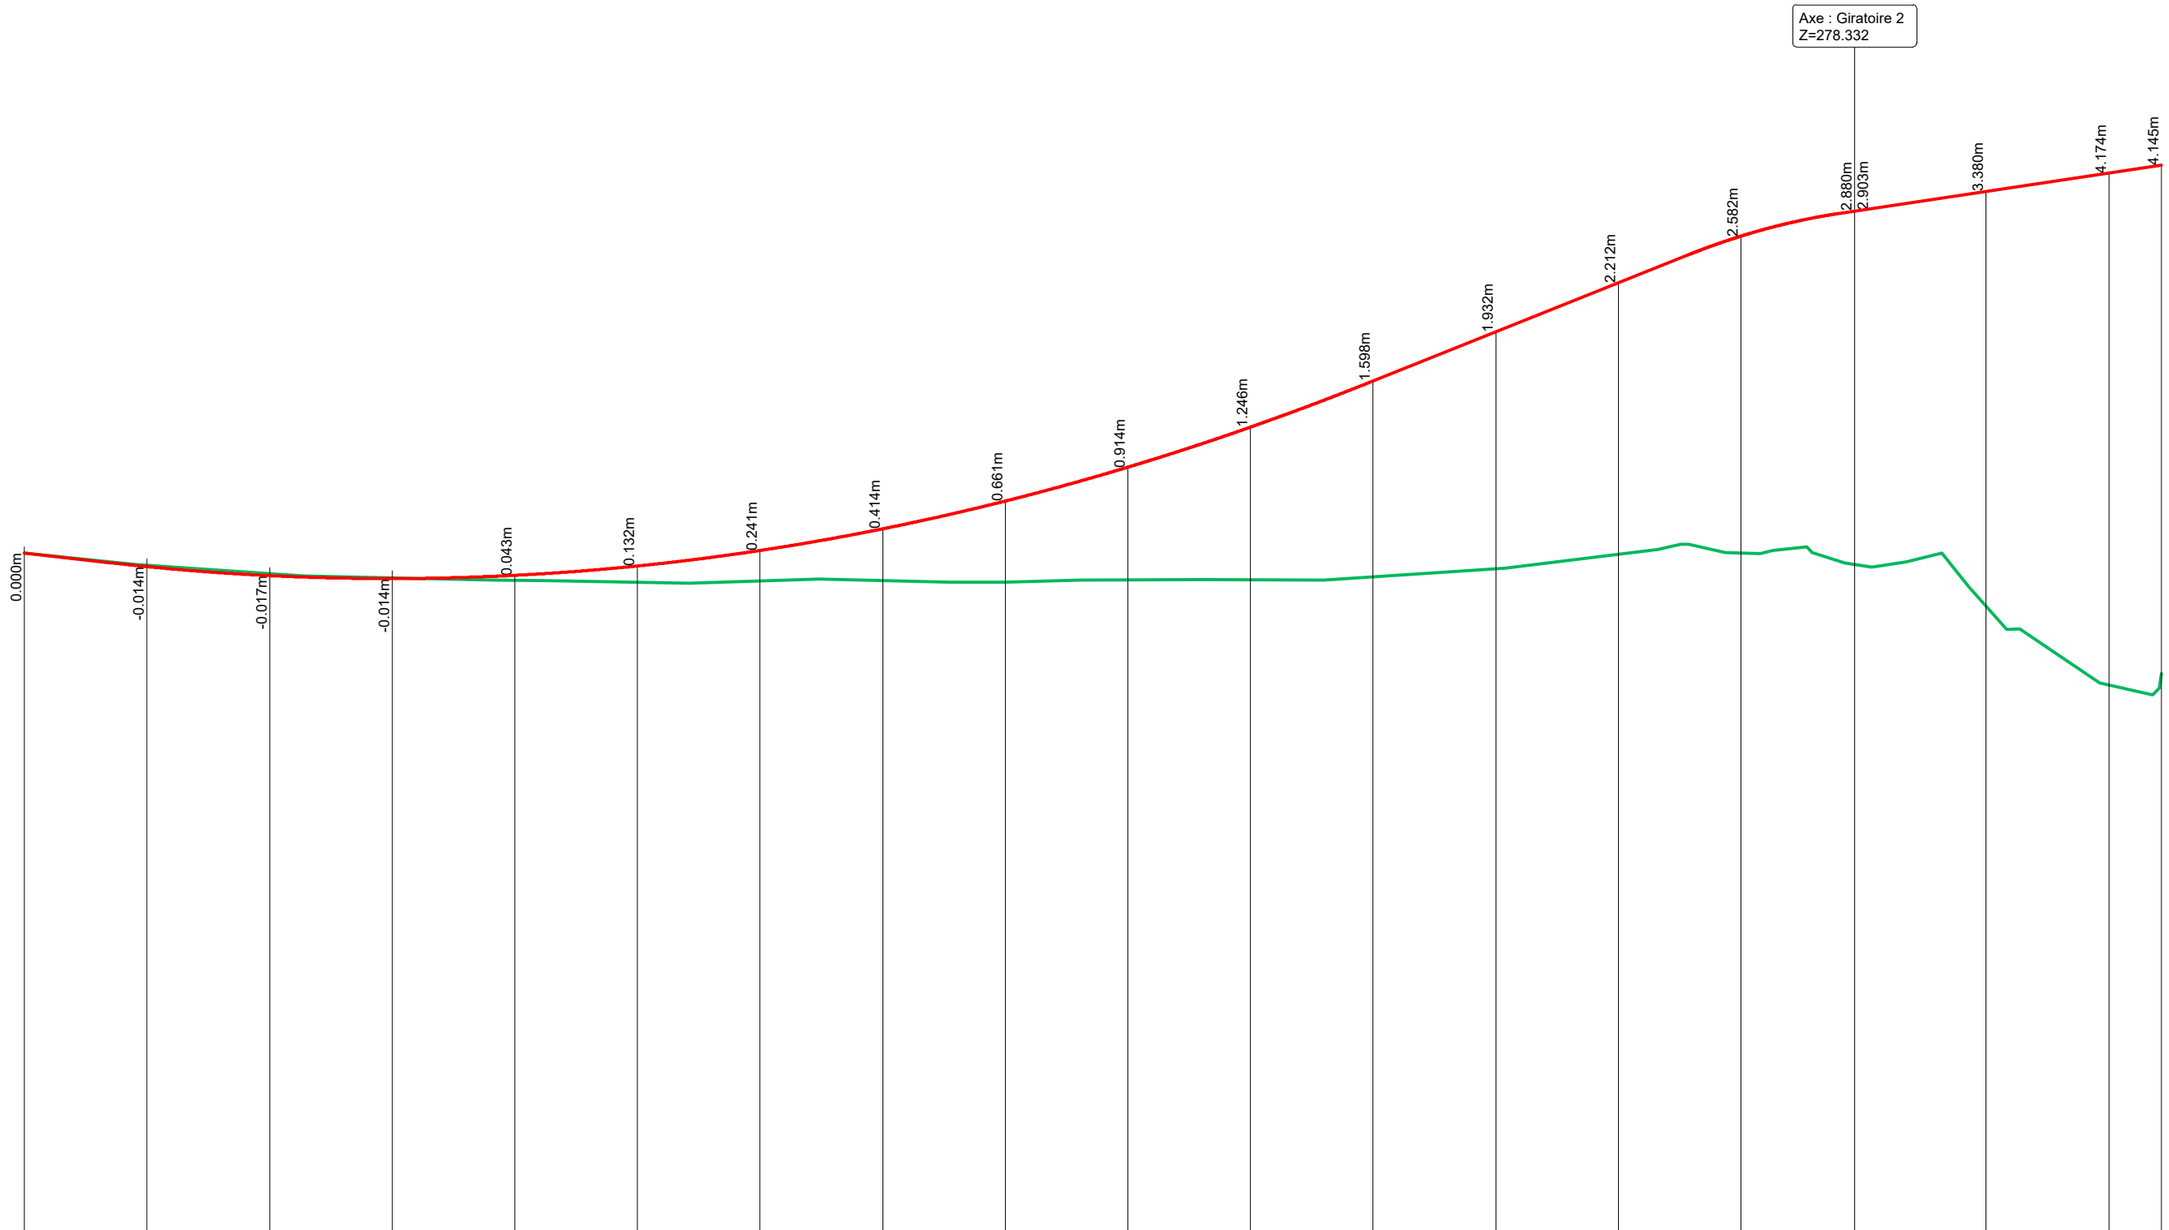

Axe : Route de Djoué

Echelle X : 1/500
Echelle Z : 1/50

Plan Comp : 270.00

Terrain	275.545	275.447	275.377	275.351	275.320	275.307	275.324	275.327	275.307	275.331	275.325	275.349	275.415	275.535	275.546	275.452	275.112	274.468	274.561
Projet Linéaire	275.545	275.434	275.360	275.336	275.363	275.439	275.565	275.742	275.968	276.244	276.571	276.947	277.347	277.747	278.127	278.332	278.492	278.642	278.707
Distances cumulées	0	10	20	30	40	50	60	70	80	90	100	110	120	130	140	149	160	170	174

Pentes et rampes: R = 1.13%; L = 7.035m; L = 102.721m, R = 2000.000m; L = 25.850m; P = 4.0%; L = 12.505m, R = -500.000m; L = 26.223m; P = 1.5%

Alignts. et courbes: L = 9.102m; L = 76.977m, R = 100.000m; L = 88.204m